


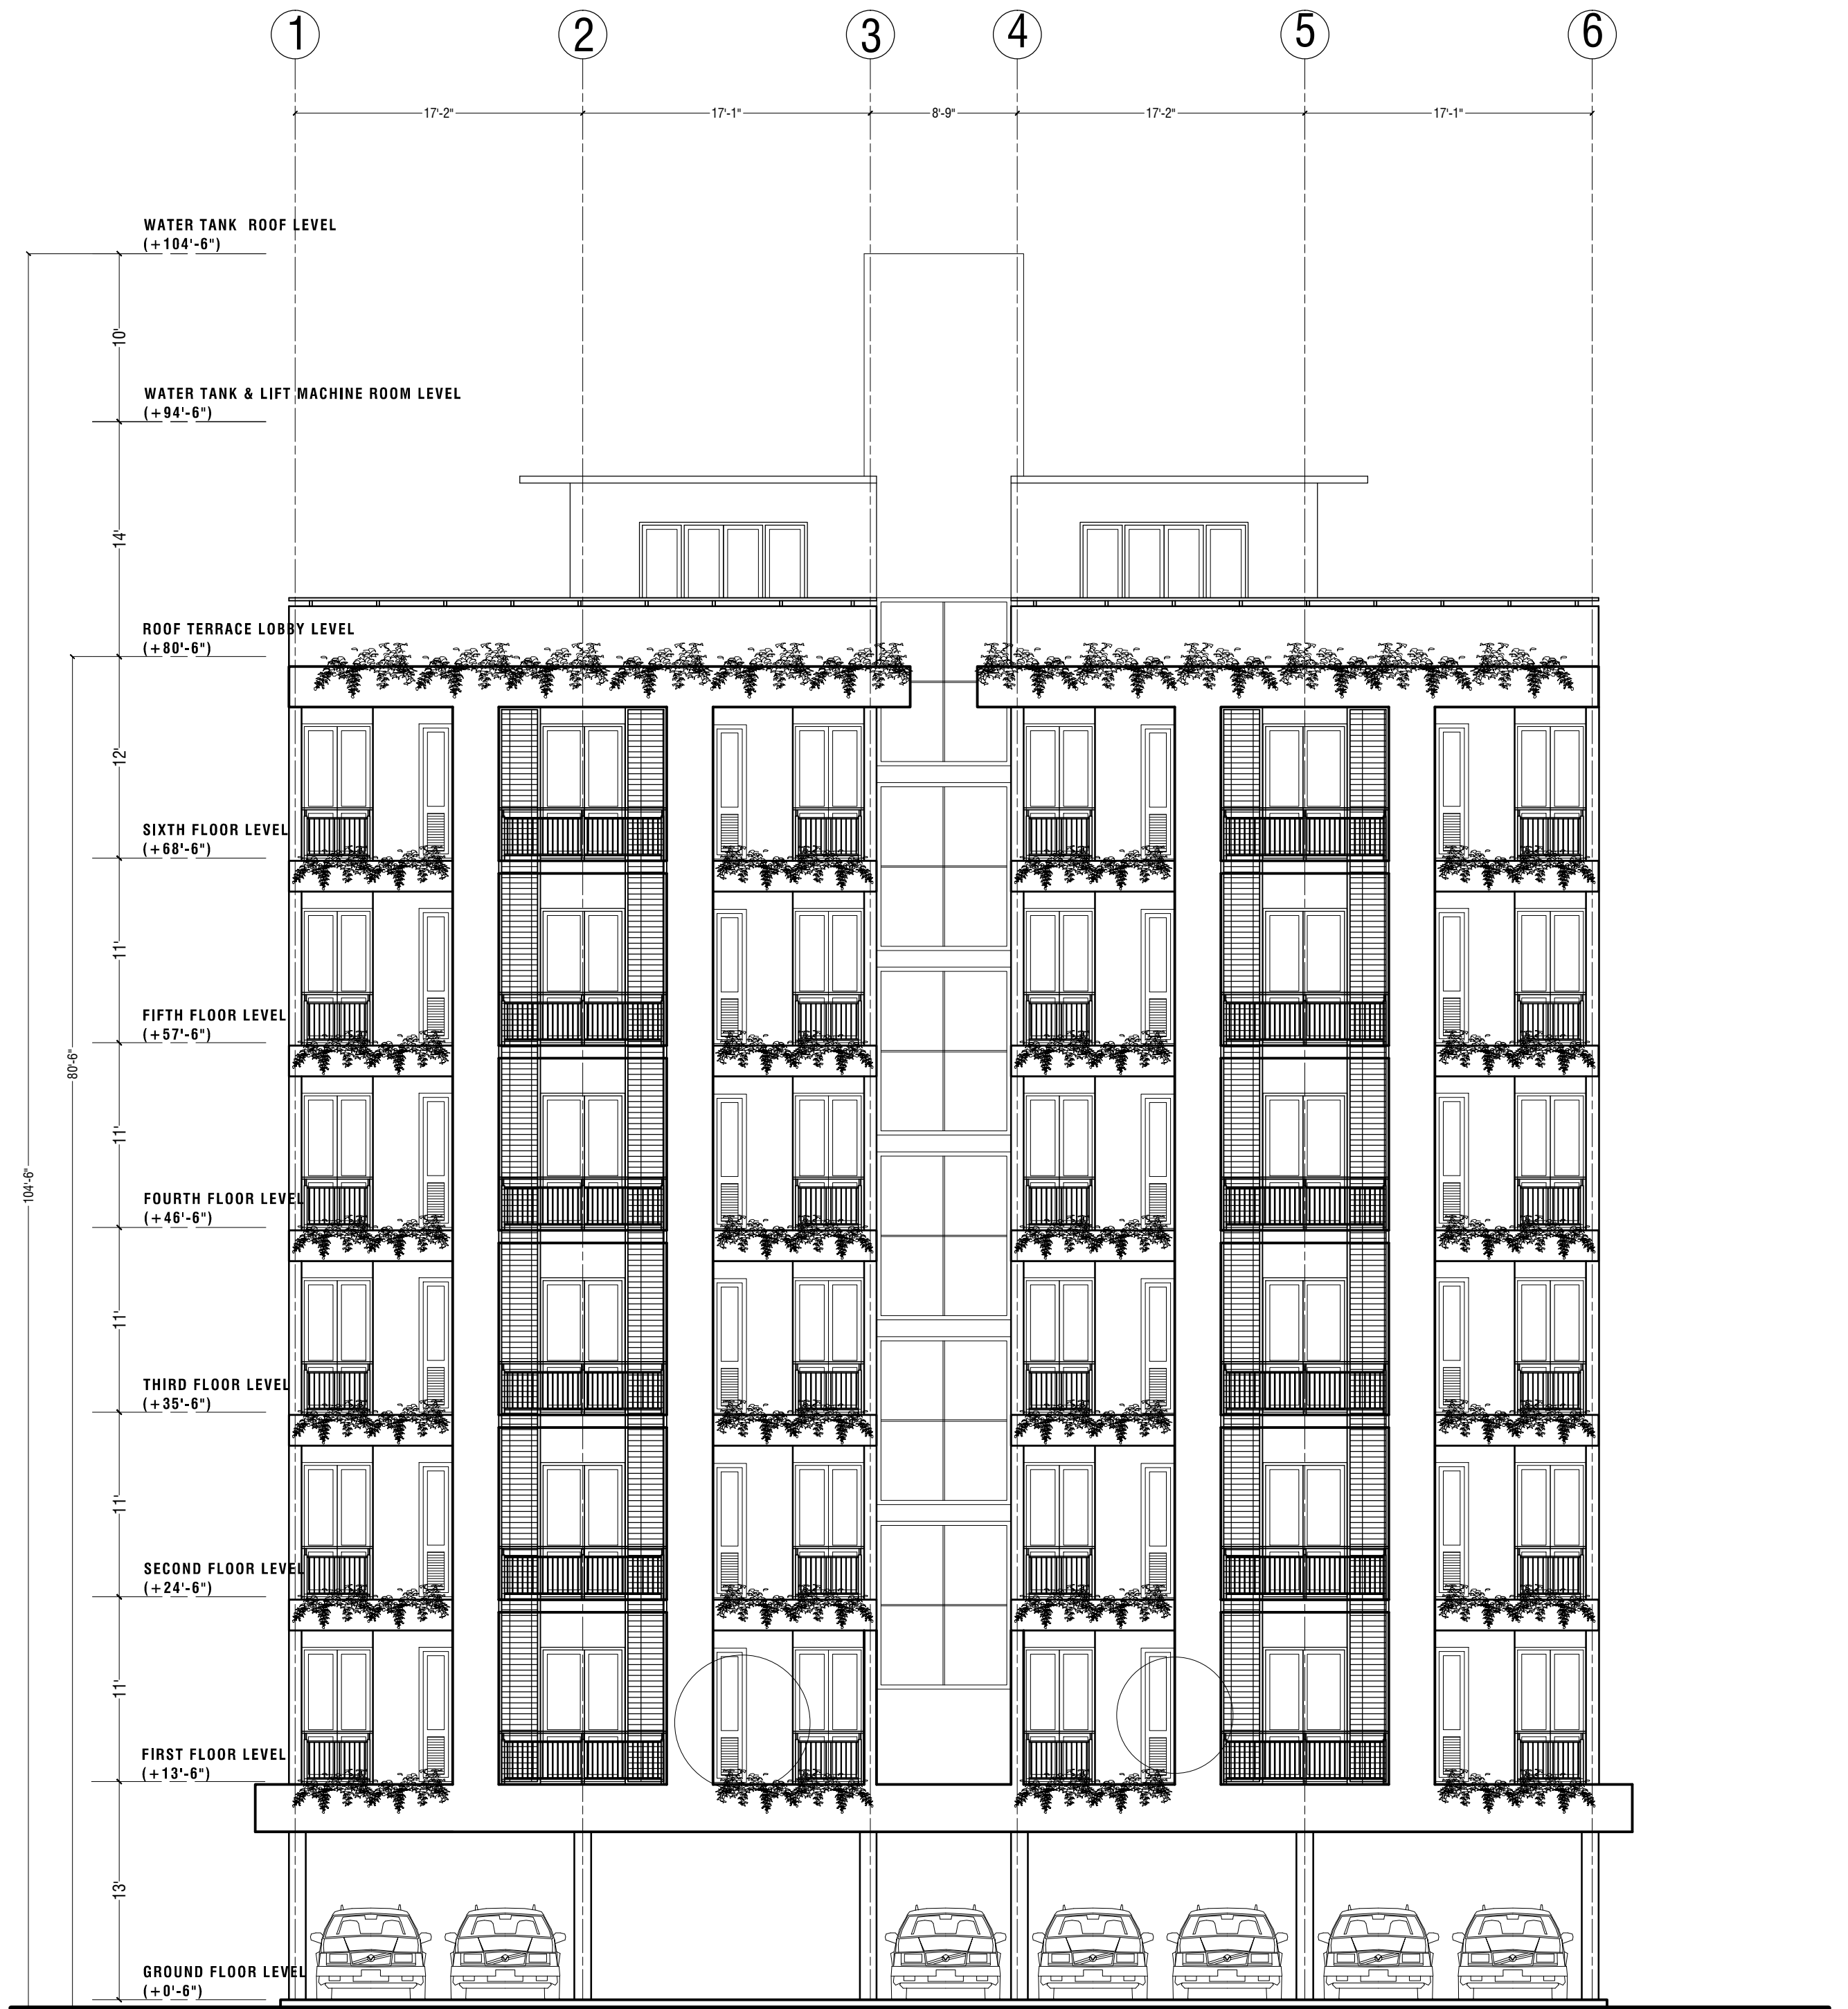

APPLICANT'S SIGNATURE

C O U N C I L D R A W I N G - B L O C K 0 2										DRAWN BY NISHATHA										PROJECT - PROPOSED APARTMENT BUILDING FOR PRIME HOMES (PVT) LTD.																			
DRAWING TITLE: PROPOSED APARTMENT COMPLEX AT MATHEGODA. 02 BED ROOM APARTMENT -FRONT ELEVATION										DATE 2017-08-31																													
										SCALE EIGHT FEET TO AN INCH																													
DWG NO: PRIME LAND/MATHEGODA/COUNCIL/02 BED ROOM APARTMENT -FRONT ELEVATION/AR /08										PAGE NO: 08					CHECKED ANIL KUMARAGE										NO:75, D.S SENANAYAKA ROAD, COLOMBO 08.														
										PAPER SIZE -A2					REVISION																								
ANIL KUMARAGE, CHARTERED ARCHITECTS, 409/2,3rd Lane, RoBUR:1 Gunawardana Mawatha, Battaramulla. Sri Lanka. Tel- 0714811625, 011-2868803. Email- akarchiteam@gmail.com. Fax- 0112868803. All Designs and Drawings are the property of Anil Kumarage, and cannot be copied or used in any way without expressed permission.																														AT LOT NO: MATHEGODA.									



SIDE ELEVATION

SCALE : EIGHT FEET TO AN INCH

ARCHITECT'S SIGNATURE

ENGINEER'S SIGNATURE

APPLICANT'S SIGNATURE

C O U N C I L D R A W I N G - B L O C K 0 2

DRAWING TITLE: PROPOSED APARTMENT COMPLEX AT MATHEGODA.
02 BED ROOM APARTMENT -SIDE ELEVATION

DWG NO:
PRIME LAND/MATHEGODA/COUNCIL/02 BED ROOM APARTMENT -SIDE ELEVATION/AR /09

PAGE NO: 09

PAPER SIZE -A2

DRAWN BY NISHATHA

DATE 2017-08-31

SCALE EIGHT FEET TO AN INCH

CHECKED ANIL KUMARAGE

REVISION

PROJECT-

PROPOSED APARTMENT BUILDING
FOR PRIME HOMES (PVT) LTD.

NO:75, D.S SENANAYAKA ROAD,
COLOMBO 08.

AT LOT NO:
MATHEGODA.

ANIL KUMARAGE, CHARTERED ARCHITECTS, 409/2,3rd Lane, RoBUR:1 Gunawardana Mawatha, Battaramulla, Sri Lanka.
Tel- 0714811625, 011-2868803. Email- akarchileam@gmail.com. Fax- 0112868803. All Designs and Drawings are the property of Anil Kumarage, and cannot be copied or used in any way without expressed permission.

D O O R W I N D O W S C H E D U L E

TYPE	LOCATION	NOS								OPENING SIZE	SILL HEIGHT	LINTEL HEIGHT	DESCRIPTION
		ground	1st	2ND	3RD	4TH	5TH	6TH	TERRACE				
D1	ENTRANCE	-	06	06	06	06	06	06	-	4'-0" x 7'-0"	-	7'-0"	TIMBER PANELED DOOR
D2	BED ROOM	-	12	12	12	12	12	12	-	3'-0" x 7'-0"	-	7'-0"	TIMBER FRAMED SOLID DOOR
D2'	GARBAGE	01	-	-	-	-	-	-		3'-0" x 8'-0"	-	8'-0"	TIMBER FRAMED SOLID DOOR
D3	TOILETS	-	12	12	12	12	12	12	-	2'-9" x 7'-0"	-	7'-0"	TIMBER FRAMED SOLID DOOR
D5	DISABLE TOILET	-	-	-	-	-	-	-	-	3'-3" x 8'-0"	-	8'-0"	TIMBER FRAMED SOLID DOOR
D6	DUCT	-	14	14	14	14	14	14	02	2'-0" x 6'-0"	1'-0"	7'-0"	ALUMINUM FRAMED COMPOSITE PANEL DOOR
D7	DUCT	01	02	02	02	02	02	02	02	4'-0" x 6'-0"	1'-0"	7'-0"	ALUMINUM FRAMED COMPOSITE PANEL DOOR
D8	DUCT	01	-	-	-	-	-	-	-	2'-10" x 6'-0"	1'-0"	7'-0"	ALUMINUM FRAMED COMPOSITE PANEL DOOR
FG	STAIRCASE	-	01	01	01	01	01	01	-	8'-0" x 8'-0"	-	8'-0"	ALUMINUM FRAMED GLAZED WINDOW
FG1	STAIRCASE LOBBY	-	02	02	02	02	02	02	-	4'-0" x 8'-0"	-	8'-0"	ALUMINUM FRAMED GLAZED WINDOW
SL	LOBBY	-	-	-	-	-	-	-	02	6'-0" x 8'-0"	-	8'-0"	ALUMINUM FRAMED SLIDING WINDOW
SL1	LIVING/DINING & PANTRY	-	02	02	02	02	02	02	-	6'-2" x 8'-0"	-	8'-0"	ALUMINUM FRAMED SLIDING WINDOW
SL2	GYM/CONDOMINIUM ROOM	-	-	-	-	-	-	-	08	10'-0" x 8'-0"	-	8'-0"	ALUMINUM FRAMED SLIDING WINDOW
FW1	LIVING/DINING & PANTRY	-	04	04	04	04	04	04	-	5'-0" x 8'-0"	-	8'-0"	ALUMINUM FRAMED FRENCH WINDOW
FW2	BED ROOM	-	12	12	12	12	12	12	-	4'-3" x 8'-0"	-	8'-0"	ALUMINUM FRAMED FRENCH WINDOW
LW	TOILET	-	12	12	12	12	12	12	-	2'-0" x 8'-0"	-	8'-0"	ALUMINUM FRAMED LOWERED WINDOW
LW1	WATER TANK	-	-	-	-	-	-	-	01	10'-3" x 7'-0"	-	7'-0"	ALUMINUM FRAMED LOUVERED WINDOW
GD	PANEL ROOM	01	-	-	-	-	-	-	-	4'-0" x 8'-0"	-	8'-0"	G.I. GATE
RD	TRANSFORMER	-	-	-	-	-	-	-	-	8'-0" x 8'-0"	-	8'-0"	ROLLER DOOR

UNIT FLOOR AREA'S

FIRST FLOOR		
UNIT 01 (TYPE A)		805 Sq. ft.
UNIT 02 (TYPE B)		847 Sq. ft.
UNIT 03 (TYPE C)		805 Sq. ft.
UNIT 04 (TYPE D)		805 Sq. ft.
UNIT 05 (TYPE E)		847 Sq. ft.
UNIT 06 (TYPE F)		805 Sq. ft.


SECOND FLOOR		
UNIT 07 (TYPE A)		805 Sq. ft.
UNIT 08 (TYPE B)		847 Sq. ft.
UNIT 09 (TYPE C)		805 Sq. ft.
UNIT 10 (TYPE D)		805 Sq. ft.
UNIT 11 (TYPE E)		847 Sq. ft.
UNIT 12 (TYPE F)		805 Sq. ft.

THIRD FLOOR		
UNIT 13 (TYPE A)		805 Sq. ft.
UNIT 14 (TYPE B)		847 Sq. ft.
UNIT 15 (TYPE C)		805 Sq. ft.
UNIT 16 (TYPE D)		805 Sq. ft.
UNIT 17 (TYPE E)		847 Sq. ft.
UNIT 18 (TYPE F)		805 Sq. ft.


FOURTH FLOOR		
UNIT 19 (TYPE A)		805 Sq. ft.
UNIT 20 (TYPE B)		847 Sq. ft.
UNIT 21 (TYPE C)		805 Sq. ft.
UNIT 22 (TYPE D)		805 Sq. ft.
UNIT 23 (TYPE E)		847 Sq. ft.
UNIT 24 (TYPE F)		805 Sq. ft.

SIXTH FLOOR		
UNIT 31 (TYPE A)		805 Sq. ft.
UNIT 32 (TYPE B)		847 Sq. ft.
UNIT 33 (TYPE C)		805 Sq. ft.
UNIT 34 (TYPE D)		805 Sq. ft.
UNIT 35 (TYPE E)		847 Sq. ft.
UNIT 36 (TYPE F)		805 Sq. ft.





FIFTH FLOOR		
UNIT 25 (TYPE A)		805 Sq. ft.
UNIT 26 (TYPE B)		847 Sq. ft.
UNIT 27 (TYPE C)		805 Sq. ft.
UNIT 28 (TYPE D)		805 Sq. ft.
UNIT 29 (TYPE E)		847 Sq. ft.
UNIT 30 (TYPE F)		805 Sq. ft.

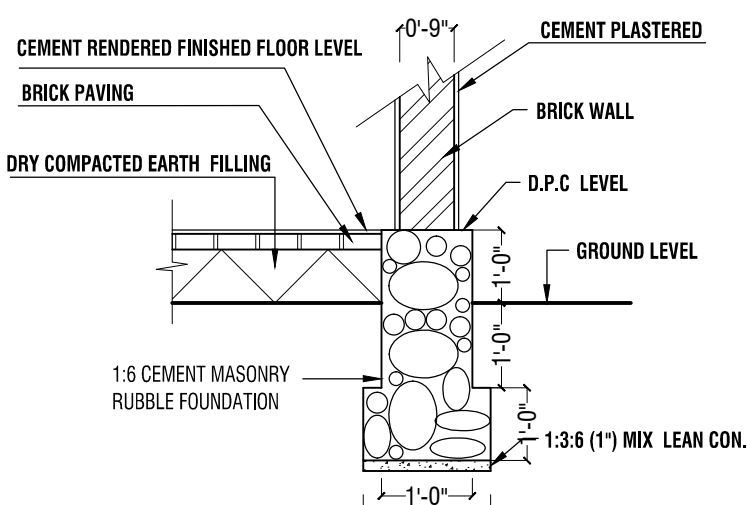


INTERNAL WALL FOUNDATION
SCALE : TWO FEET TO AN INCH

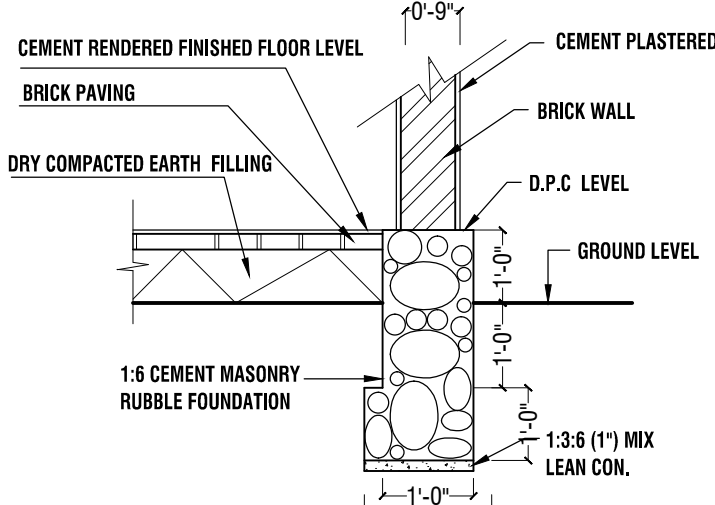

BLIND WALL FOUNDATION
SCALE : TWO FEET TO AN INCH

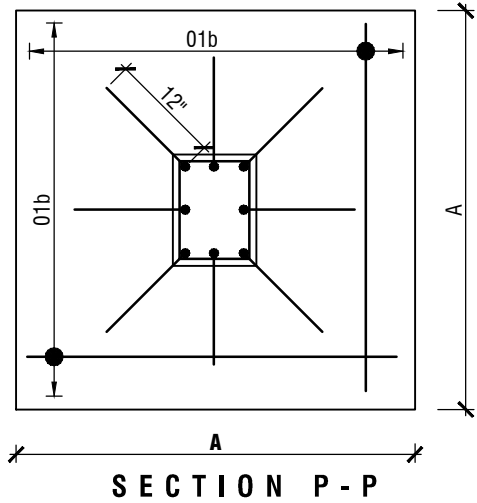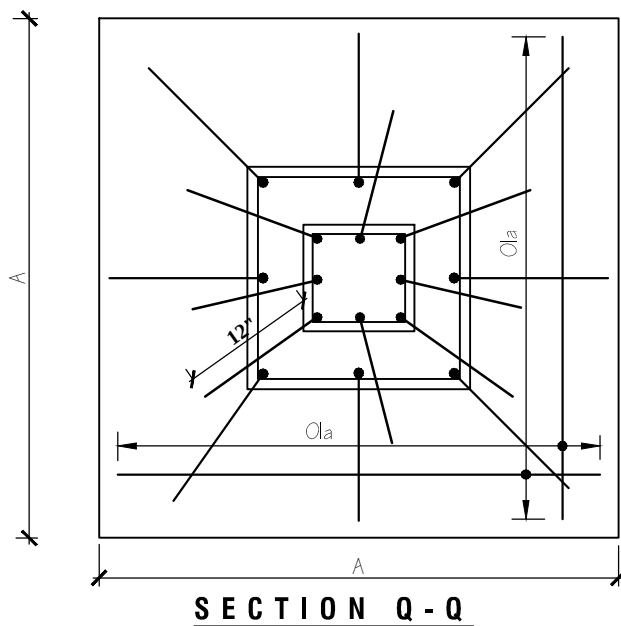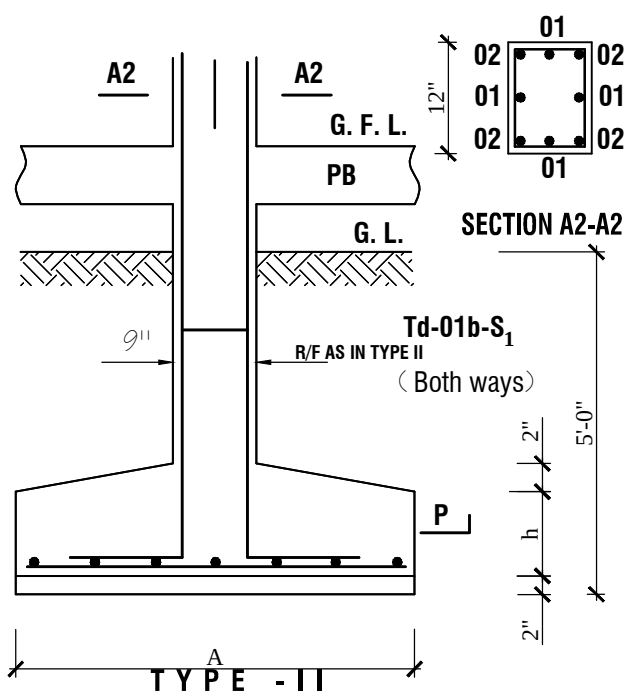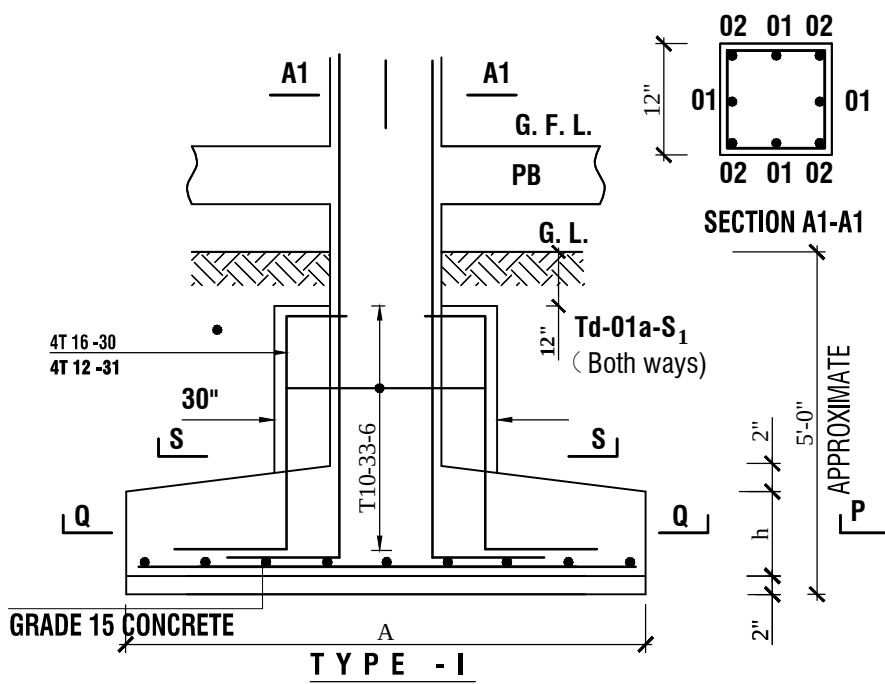

DETAILS OF COLUMNS & FOOTINGS
SCALE : NOT TO SCALE

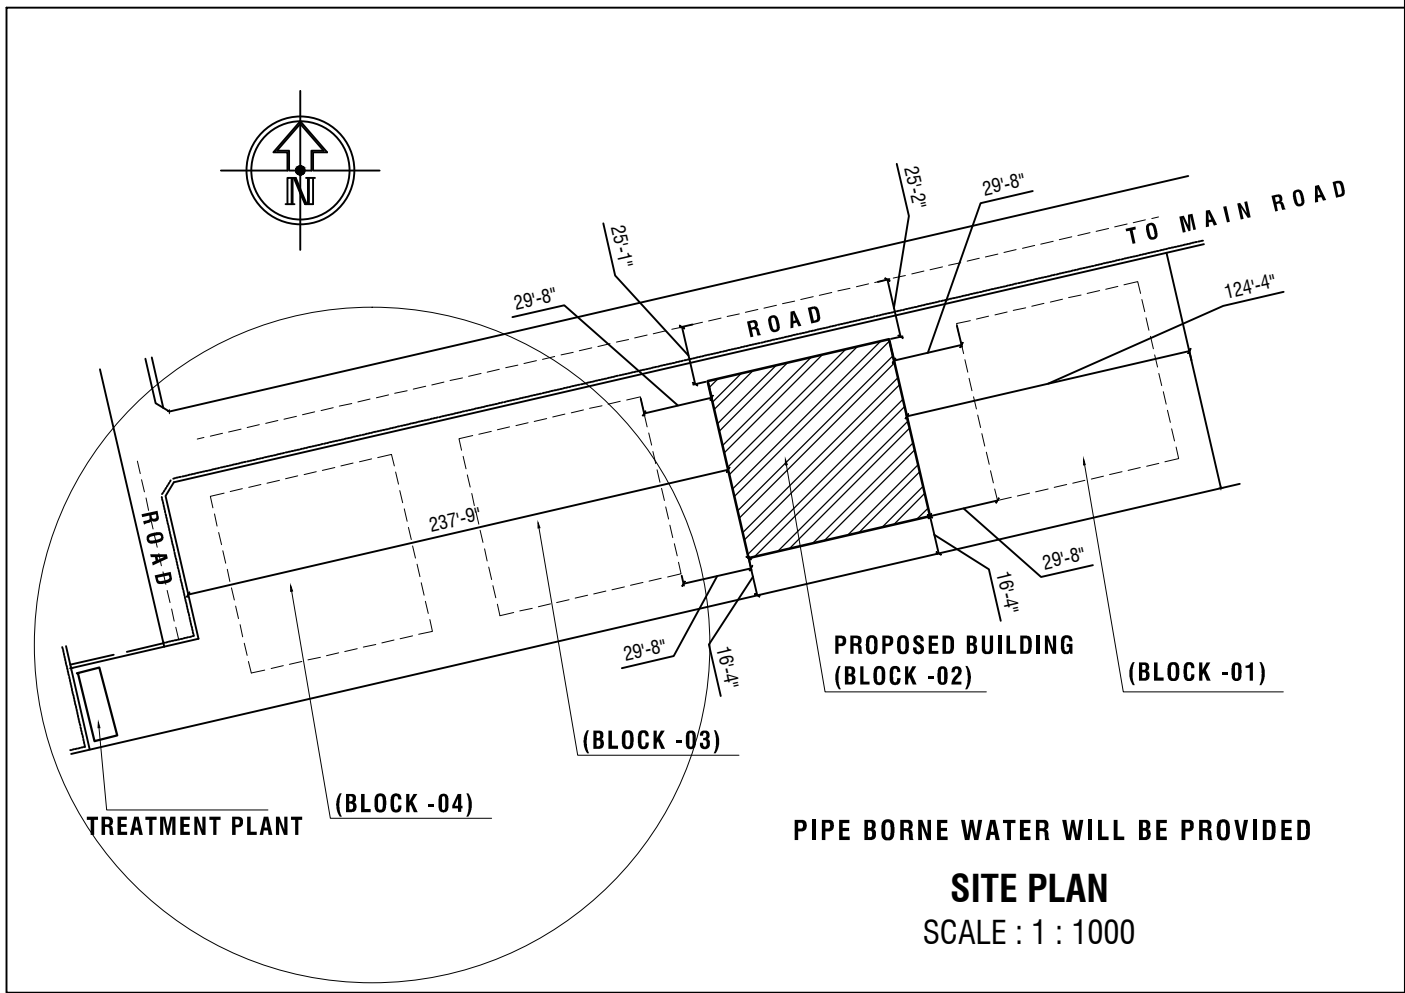

ARCHITECT'S SIGNATURE

ENGINEER'S SIGNATURE

APPLICANT'S SIGNATURE

C O U N C I L D R A W I N G - B L O C K 0 2

DRAWING TITLE: PROPOSED APARTMENT COMPLEX AT MATHEGODA.

02 BED ROOM APARTMENT -DOOR WINDOW SCHEDULE/UNIT FLOOR AREA'S/ FOUNDATION DETAIL/SITE PLAN

DWG NO:
PRIME LAND/MATHEGODA/COUNCIL/02 BED ROOM APARTMENT -SCHEDULE,LWOOR AREA'S,FOUNDATION & SITE PLAN/AR /10

PAGE NO:10

PAPER SIZE -A2

DRAWN BY NISHATHA

DATE 2017-08-31

SCALE EIGHT FEET TO AN INCH

CHECKED ANIL KUMARAGE

REVISION


PROJECT-

PROPOSED APARTMENT BUILDING
FOR PRIME HOMES (PVT) LTD.

NO:75, D.S SENANAYAKA ROAD,
COLOMBO 08.

AT LOT NO:
MATHEGODA.

ANIL KUMARAGE, CHARTERED ARCHITECTS, 409/2,3rd Lane, RoBUR:t Gunawardana Mawatha, Battaramulla. Sri Lanka.
Tel- 0714811625, 011-2868803. Email- akarchileam@gmail.com. Fax- 0112868803. All Designs and Drawings are the property of Anil Kumarage, and cannot be copied or used in any way without expressed permission.

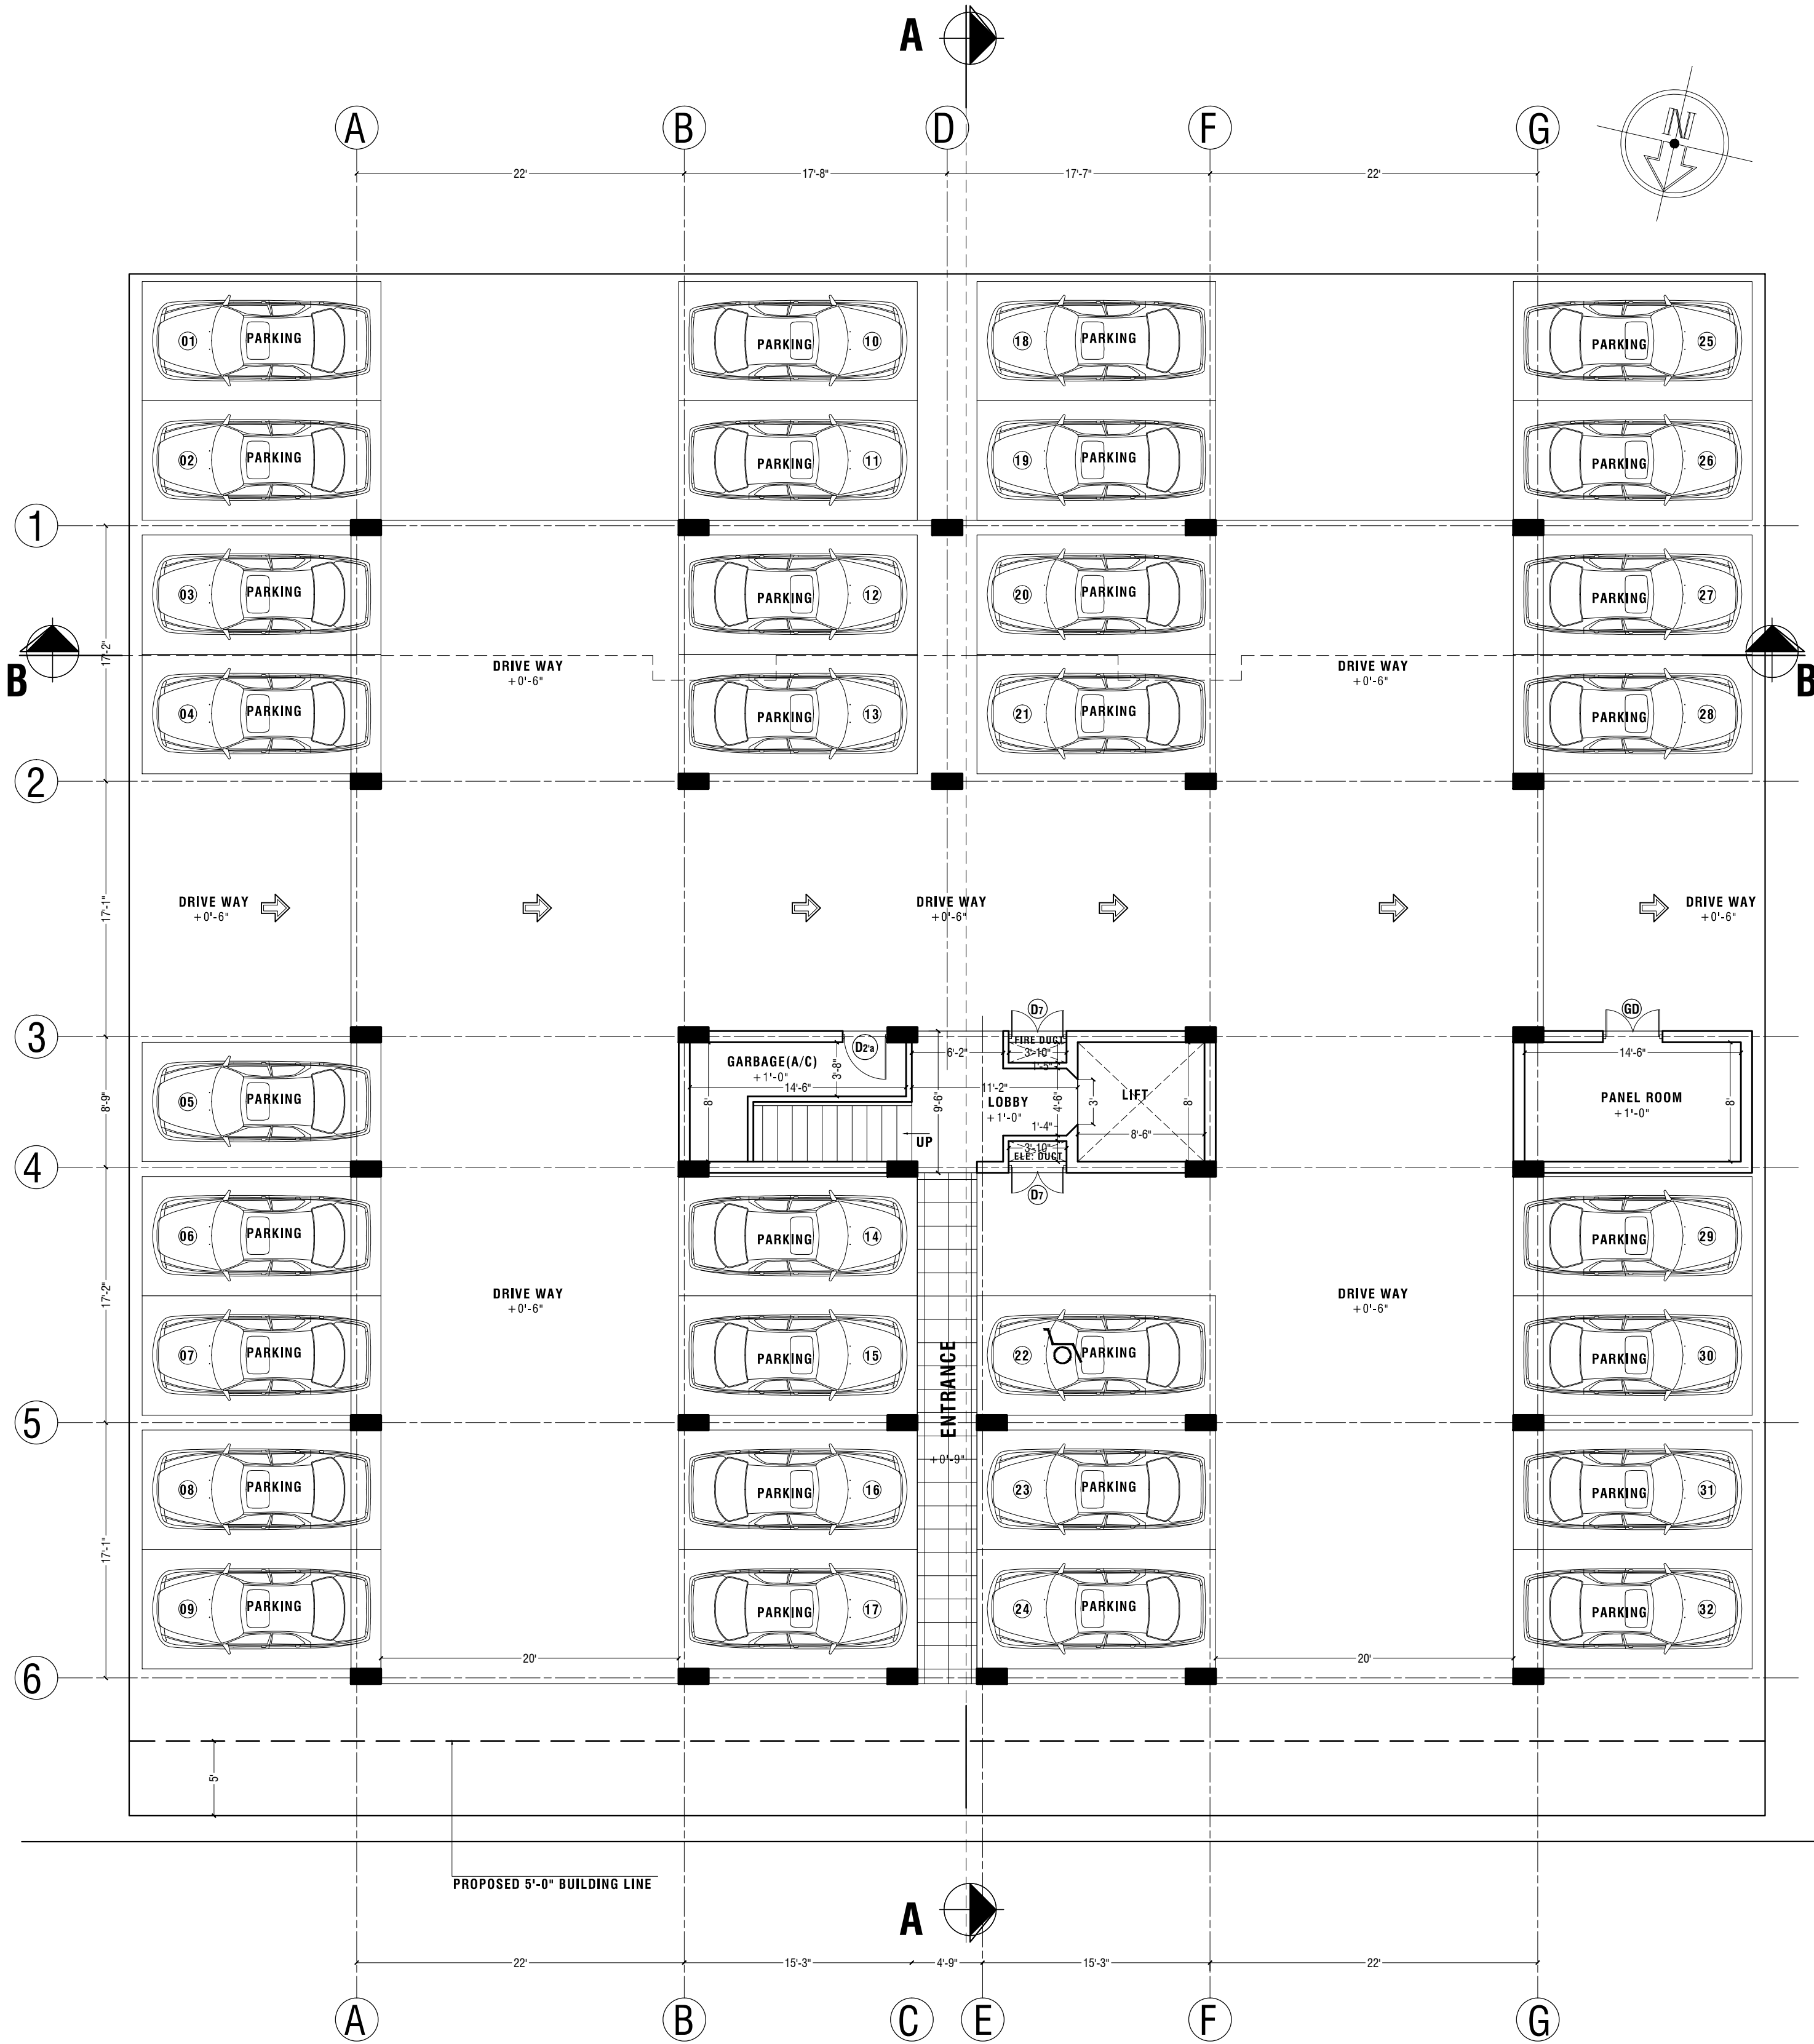

BLOCK-02,03&04(02 BED ROOM)
GROUND FLOOR PLAN
SCALE : EIGHT FEET TO AN INCH
FLOOR AREA :6233 SQ.FT

ARCHITECT'S SIGNATURE ENGINEER'S SIGNATURE APPLICANT'S SIGNATURE

C O U N C I L D R A W I N G - B L O C K 0 2					DRAWN BY NISHATHA										PROJECT- PROPOSED APARTMENT BUILDING FOR PRIME HOMES (PVT) LTD. NO:75, D.S SENANAYAKA ROAD, COLOMBO 08. AT LOT NO: MATHEGODA.
DRAWING TITLE: PROPOSED APARTMENT COMPLEX AT MATHEGODA. 02 BED ROOM APARTMENT -GROUND FLOOR PLAN					DATE					2017-08-31					
					SCALE					EIGHT FEET TO AN INCH					
DWG NO: PRIME LAND/MATHEGODA/COUNCIL/02 BED ROOM APARTMENT -TYPICAL FLOOR PLAN/AR /01					PAGE NO: 01		CHECKED ANIL KUMARAGE								
					PAPER SIZE -A2		REVISION								
ANIL KUMARAGE, CHARTERED ARCHITECTS, 409/2,3rd Lane, RoBUR:t Gunawardana Mawatha, Battaramulla. Sri Lanka. Tel- 0714811625, 011-2868803. Email- akarchiteam@gmail.com. Fax- 0112868803. All Designs and Drawings are the property of Anil Kumarage, and cannot be copied or used in any way without expressed permission.															



FIRST FLOOR PLAN
SCALE : EIGHT FEET TO AN INCH
FLOOR AREA : 5 560 SQ.FT

ARCHITECT'S SIGNATURE

ENGINEER'S SIGNATURE

APPLICANT'S SIGNATURE

C O U N C I L D R A W I N G - B L O C K 0 2

DRAWING TITLE: PROPOSED APARTMENT COMPLEX AT MATHEGODA.
02 BED ROOM APARTMENT -FIRST FLOOR PLAN

DWG NO:
PRIME LAND/MATHEGODA/COUNCIL/02 BED ROOM APARTMENT -FIRST FLOOR PLAN/AR/02

PAGE NO: 02

PAPER SIZE -A2

DRAWN BY NISHATHA

DATE 2017-08-31

SCALE EIGHT FEET TO AN INCH

CHECKED ANIL KUMARAGE

REVISION

PROJECT-

PROPOSED APARTMENT BUILDING
FOR PRIME HOMES (PVT) LTD.

NO:75, D.S SENANAYAKA ROAD,
COLOMBO 08.

AT LOT NO:
MATHEGODA.

ANIL KUMARAGE, CHARTERED ARCHITECTS, 409/2,3rd Lane, RoBUR:t Gunawardana Mawatha, Battaramulla, Sri Lanka.
Tel- 0714811625, 011-2868803. Email- akarchileam@gmail.com. Fax- 0112868803. All Designs and Drawings are the property of Anil Kumarage, and cannot be copied or used in any way without expressed permission.



TYPICAL FLOOR PLAN
(0 2 N D , 3 R D , 4 T H , 5 T H & 6 T H)
SCALE : EIGHT FEET TO AN INCH
FLOOR AREA : 5 620 SQ.FT X05=28 100 SQ.FT

ARCHITECT'S SIGNATURE

ENGINEER'S SIGNATURE

APPLICANT'S SIGNATURE

C O U N C I L D R A W I N G - B L O C K 0 2

DRAWING TITLE: PROPOSED APARTMENT COMPLEX AT MATHEGODA.
02 BED ROOM APARTMENT -TYPICAL FLOOR PLAN

DWG NO:
PRIME LAND/MATHEGODA/COUNCIL/02 BED ROOM APARTMENT -TYPICAL FLOOR PLAN/AR /03

PAGE NO: 03

PAPER SIZE -A2

DRAWN BY NISHATHA

DATE 2017-08-31

SCALE EIGHT FEET TO AN INCH

CHECKED ANIL KUMARAGE

REVISION


PROJECT-

PROPOSED APARTMENT BUILDING
FOR PRIME HOMES (PVT) LTD.

NO:75, D.S SENANAYAKA ROAD,
COLOMBO 08.

AT LOT NO:
MATHEGODA.

ANIL KUMARAGE, CHARTERED ARCHITECTS, 409/2,3rd Lane, RoBUR:t Gunawardana Mawatha, Battaramulla, Sri Lanka.
Tel- 0714811625, 011-2868803. Email- akarchiteam@gmail.com. Fax- 0112868803. All Designs and Drawings are the property of Anil Kumarage, and cannot be copied or used in any way without expressed permission.

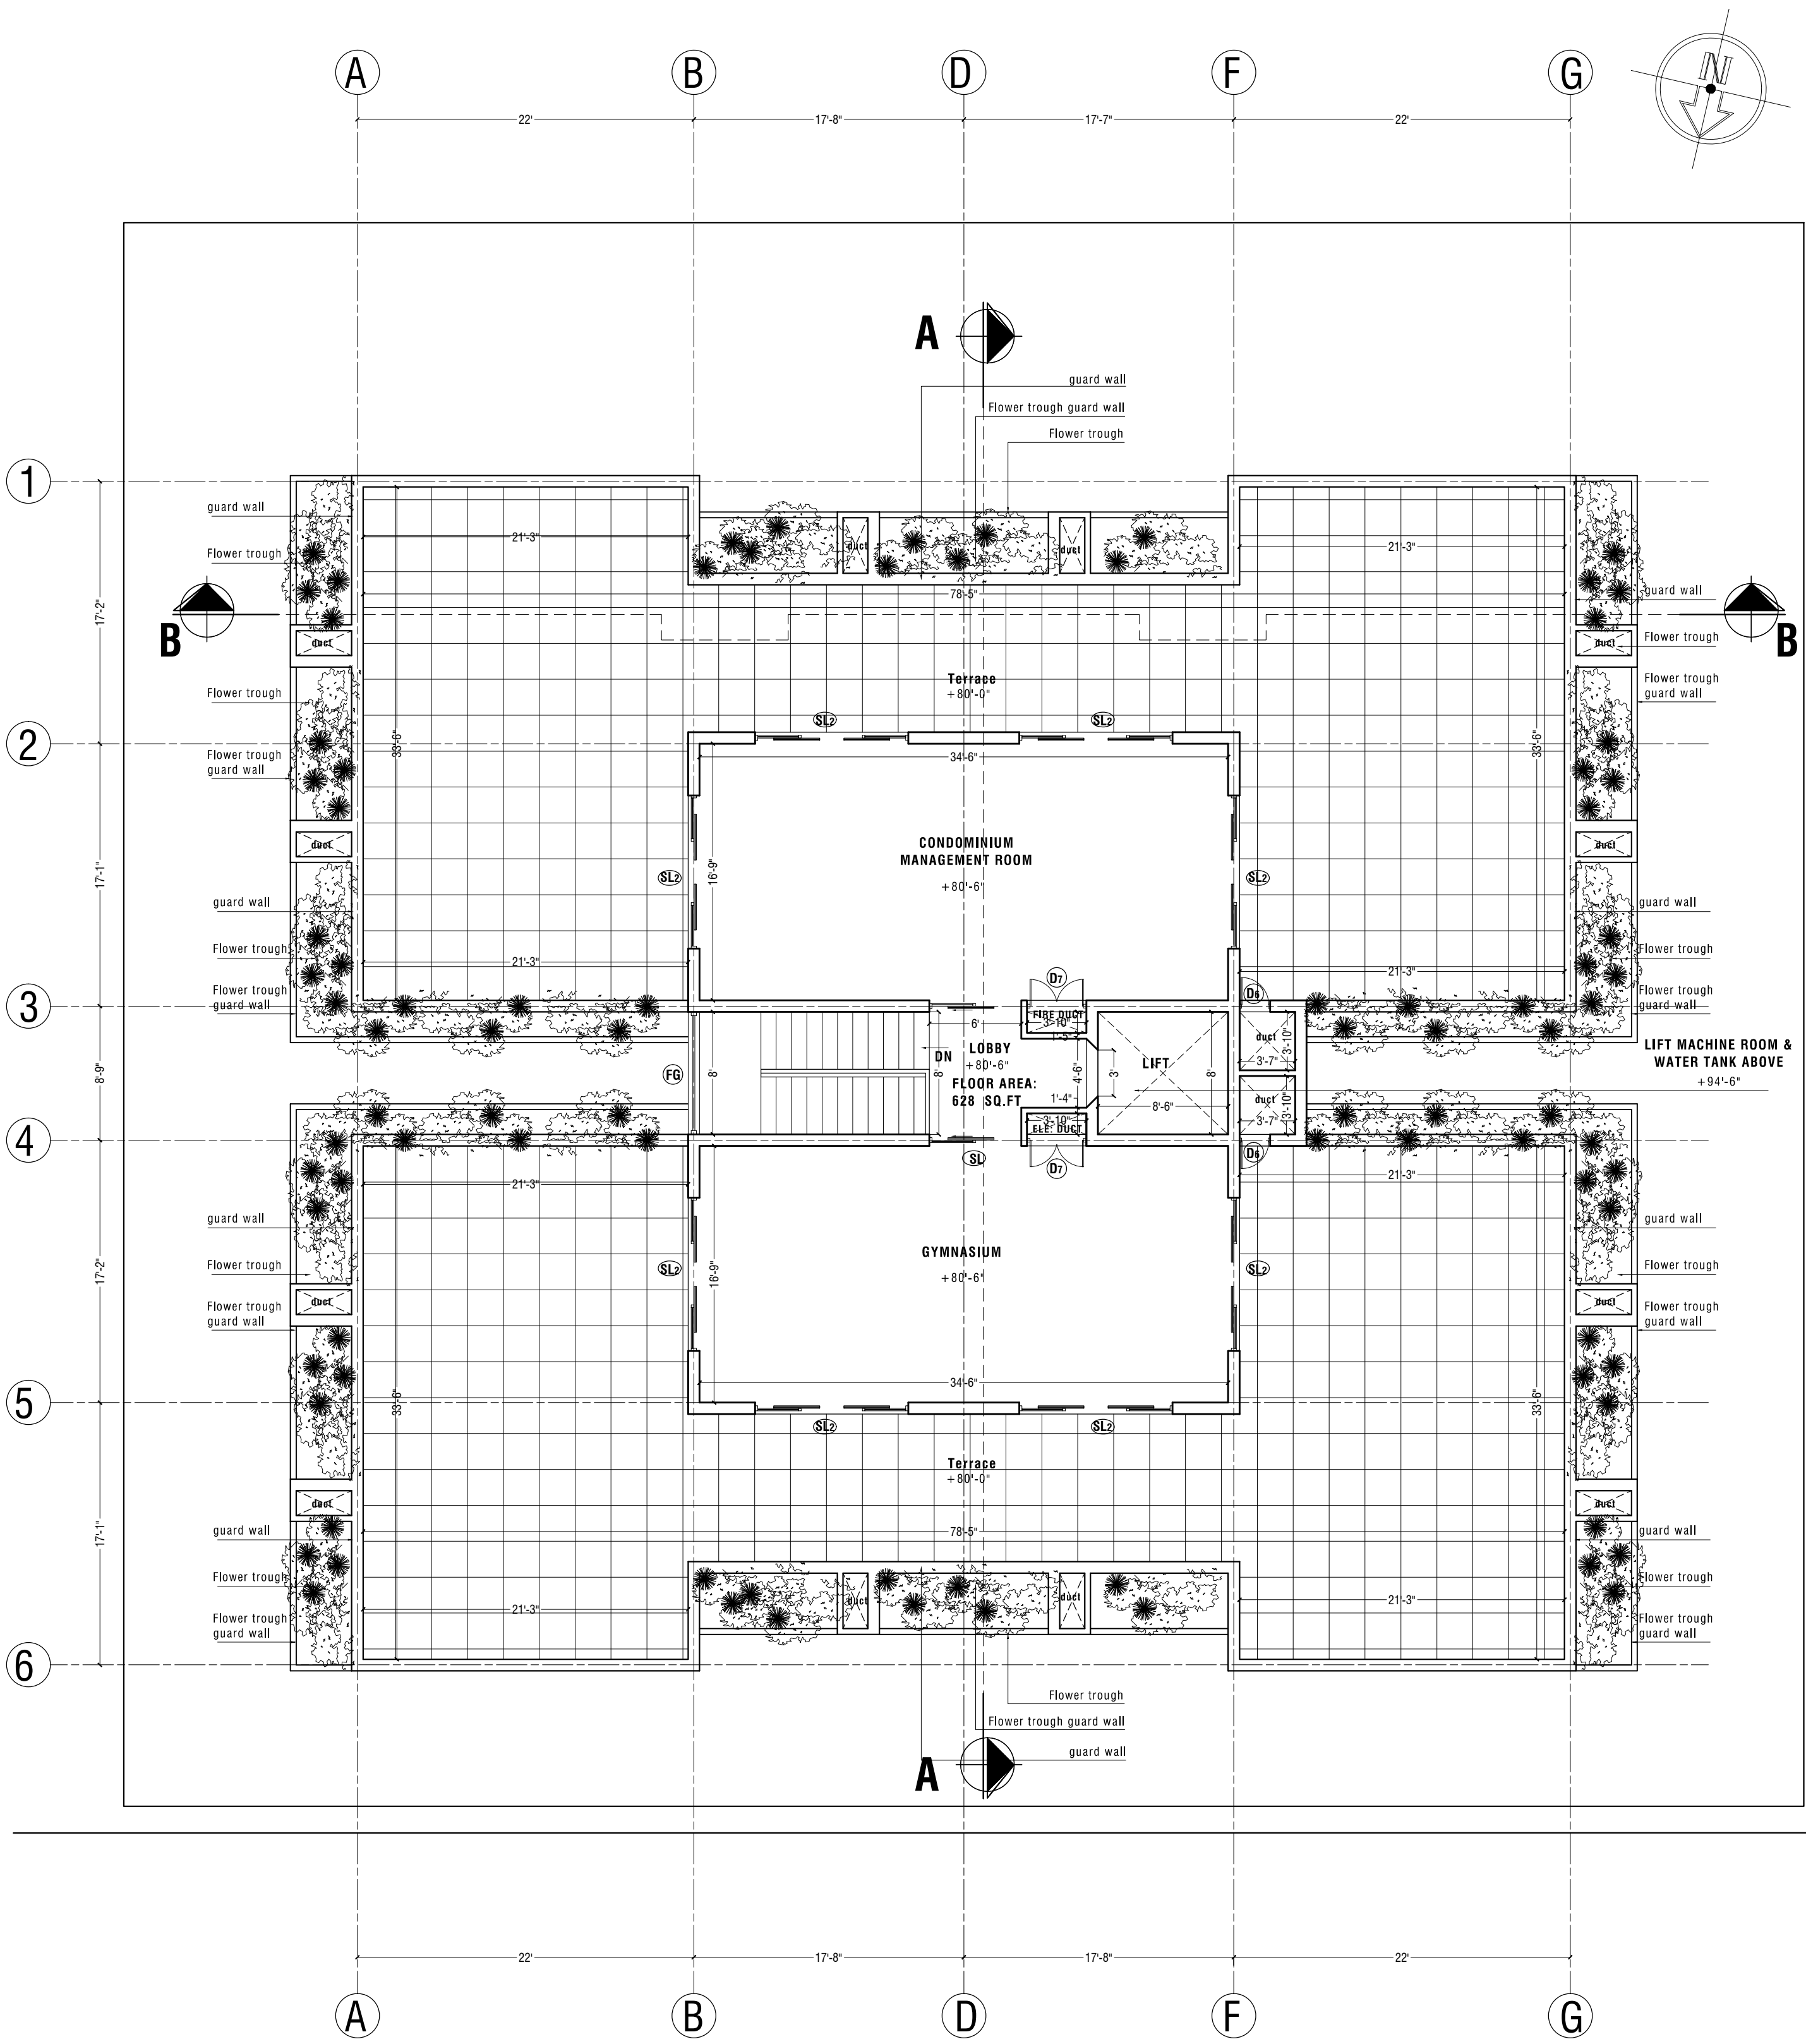


ROOF TERRACE PLAN
SCALE : EIGHT FEET TO AN INCH
FLOOR AREA :1 491 SQ.FT
ROOF TERRACE AREA:3 840 SQ.FT
FLOWER TROUGH AREA:996 SQ.FT

ARCHITECT'S SIGNATURE

ENGINEER'S SIGNATURE

APPLICANT'S SIGNATURE

C O U N C I L D R A W I N G - B L O C K 0 2					DRAWN BY NISHATHA										PROJECT- PROPOSED APARTMENT BUILDING FOR PRIME HOMES (PVT) LTD. NO:75, D.S SENANAYAKA ROAD, COLOMBO 08. AT LOT NO: MATHEGODA.
DRAWING TITLE: PROPOSED APARTMENT COMPLEX AT MATHEGODA. 02 BED ROOM APARTMENT -ROOF TERRACE PLAN					DATE 2017-08-31										
					SCALE EIGHT FEET TO AN INCH										
DWG NO: PRIME LAND/MATHEGODA/COUNCIL/02 BED ROOM APARTMENT -ROOF TERRACE PLAN/AR /04					PAGE NO: 04		CHECKED ANIL KUMARAGE								
					PAPER SIZE -A2		REVISION								
ANIL KUMARAGE, CHARTERED ARCHITECTS, 409/2,3rd Lane, RoBUR:t Gunawardana Mawatha, Battaramulla, Sri Lanka. Tel- 0714811625, 011-2868803. Email- akarchiteam@gmail.com. Fax- 0112868803. All Designs and Drawings are the property of Anil Kumarage, and cannot be copied or used in any way without expressed permission.															

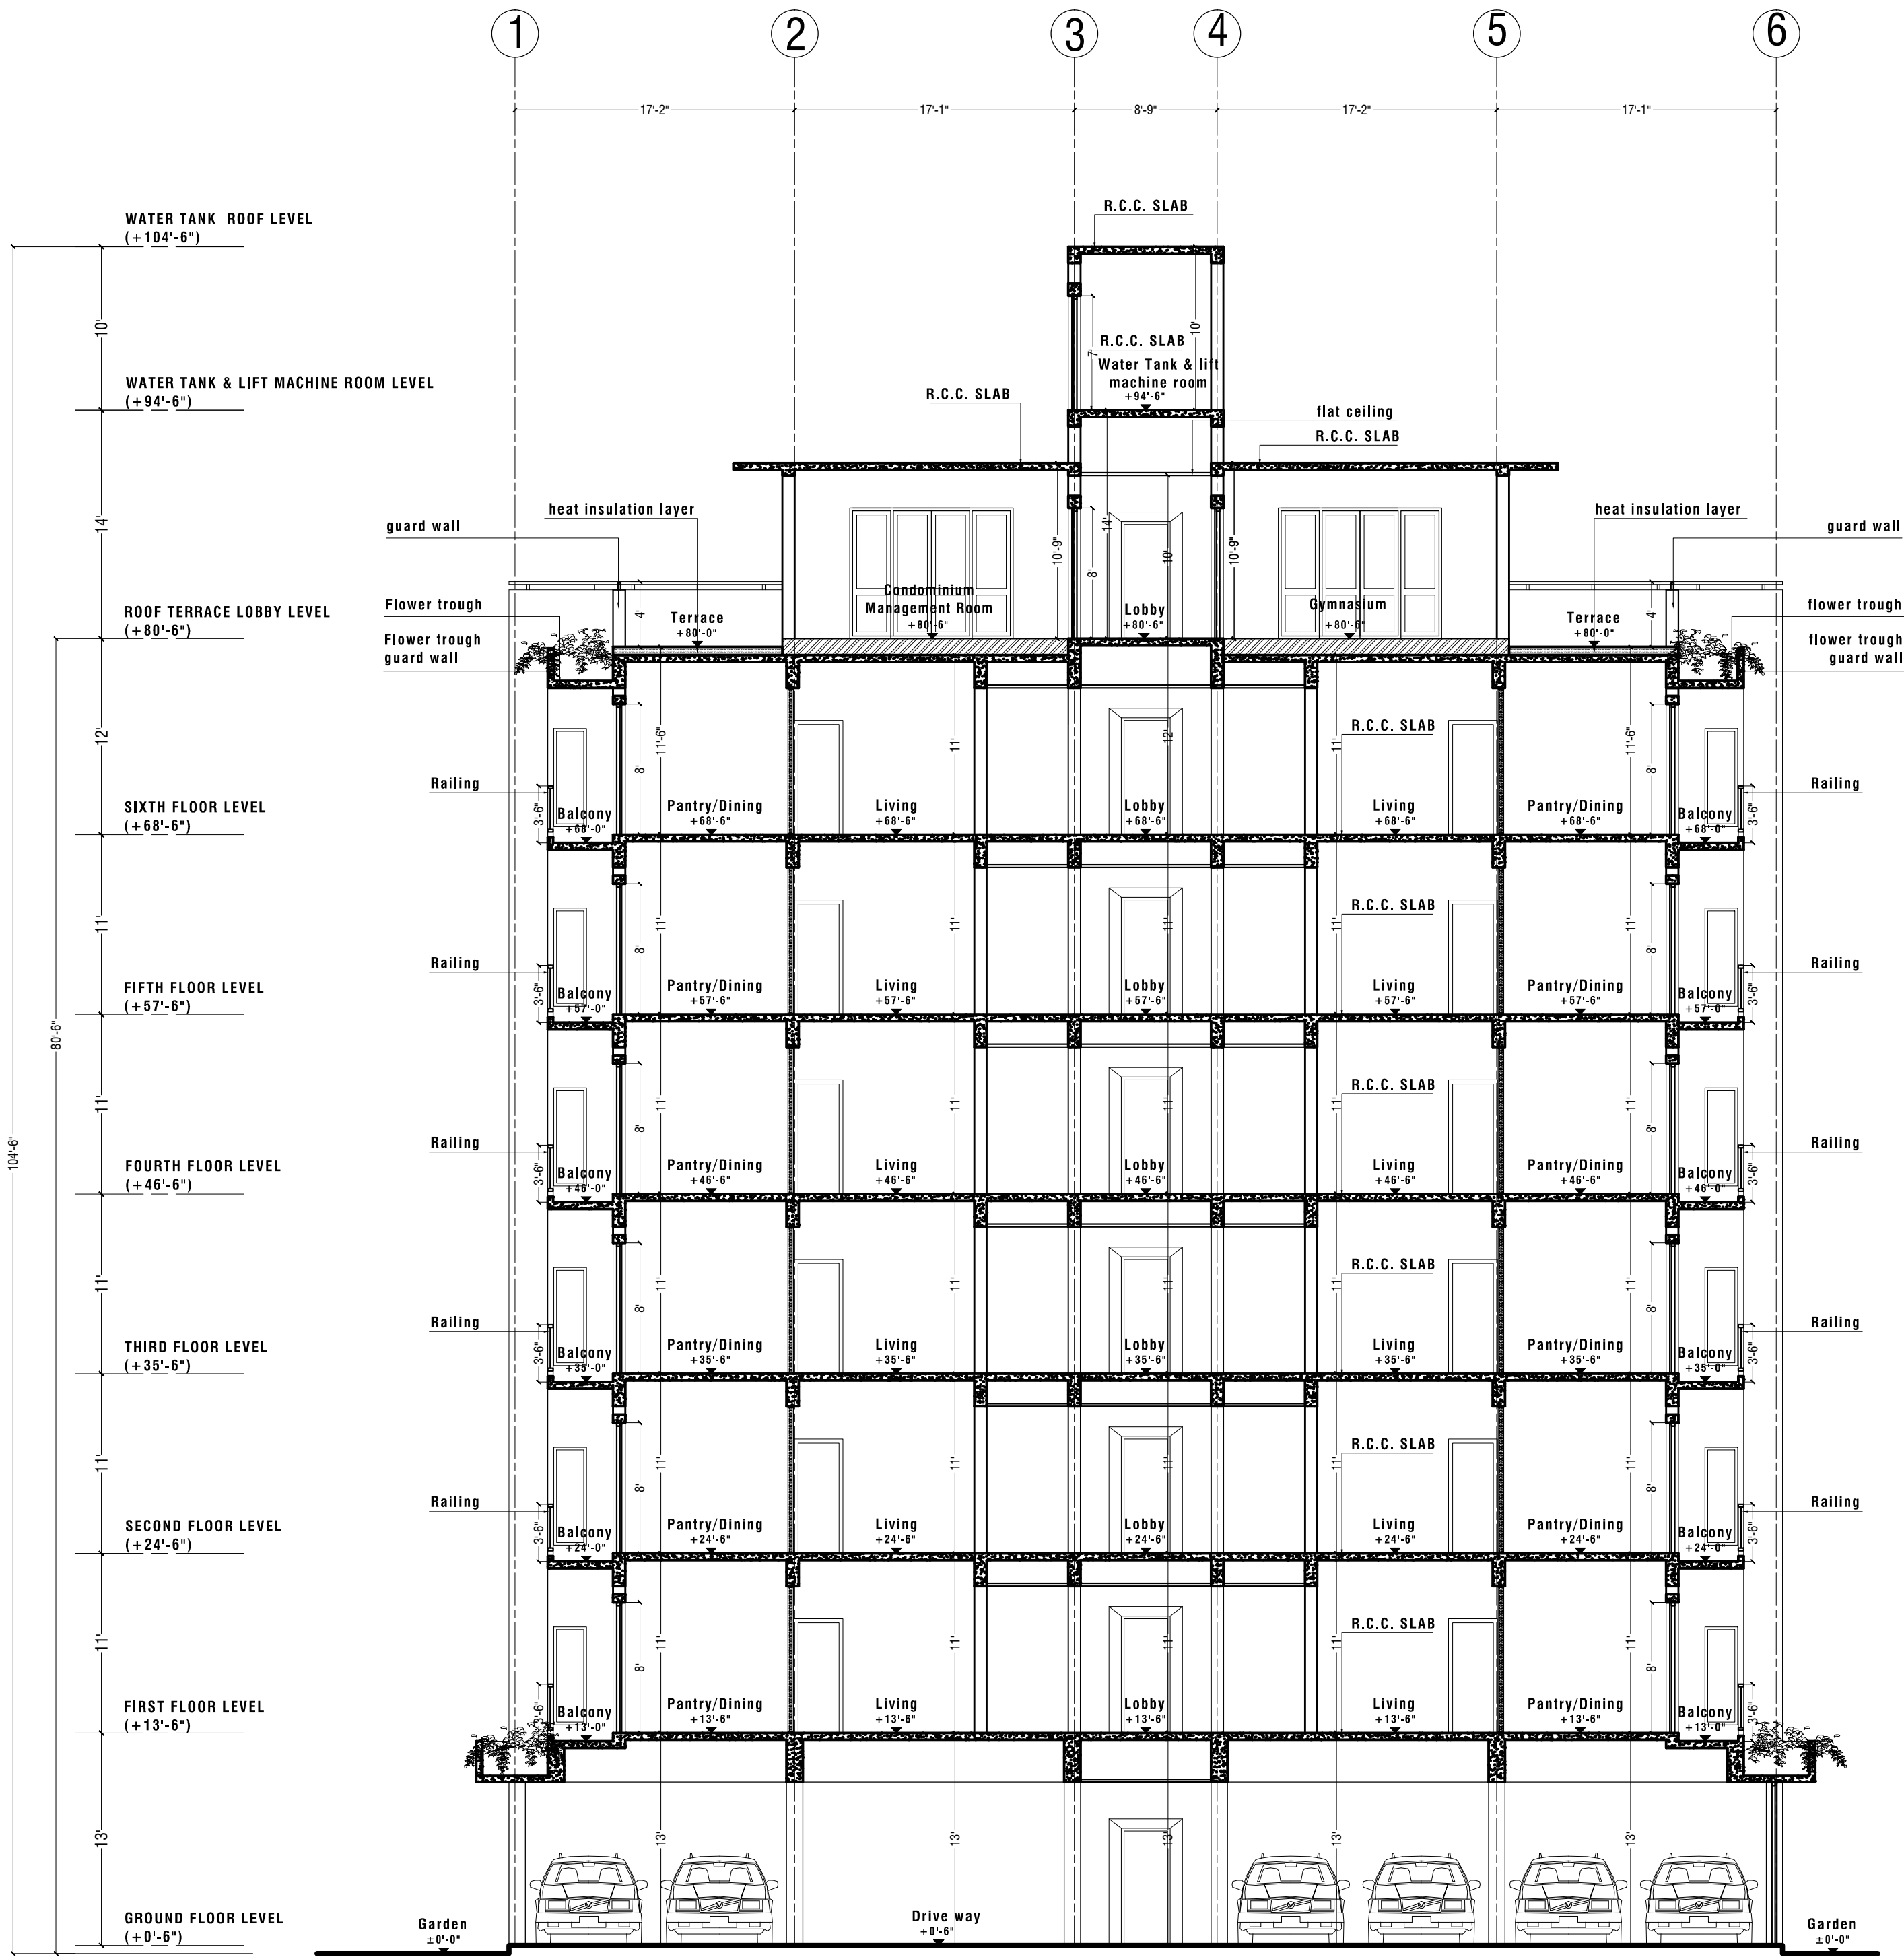

SECTIONAL ELEVATION A-A
SCALE : EIGHT FEET TO AN INCH

ARCHITECT'S SIGNATURE

ENGINEER'S SIGNATURE

APPLICANT'S SIGNATURE

C O U N C I L D R A W I N G - B L O C K 0 2					DRAWN BY NISHATHA					PROJECT- PROPOSED APARTMENT BUILDING FOR PRIME HOMES (PVT) LTD. NO:75, D.S SENANAYAKA ROAD, COLOMBO 08. AT LOT NO: MATHEGODA.						
DRAWING TITLE: PROPOSED APARTMENT COMPLEX AT MATHEGODA. 02 BED ROOM APARTMENT -SECTIONAL ELEVATION A-A					DATE 2017-08-31											
					SCALE EIGHT FEET TO AN INCH											
DWG NO: PRIME LAND/MATHEGODA/COUNCIL/02 BED ROOM APARTMENT -SECTIONAL ELEVATION A-A/AR /06					PAGE NO: 06		CHECKED ANIL KUMARAGE									
					PAPER SIZE -A2		REVISION									
ANIL KUMARAGE, CHARTERED ARCHITECTS, 409/2,3rd Lane, RoBUR:t Gunawardana Mawatha, Battaramulla, Sri Lanka. Tel- 0714811625, 011-2868803. Email- akarchiteam@gmail.com. Fax- 0112868803. All Designs and Drawings are the property of Anil Kumarage, and cannot be copied or used in any way without expressed permission.																